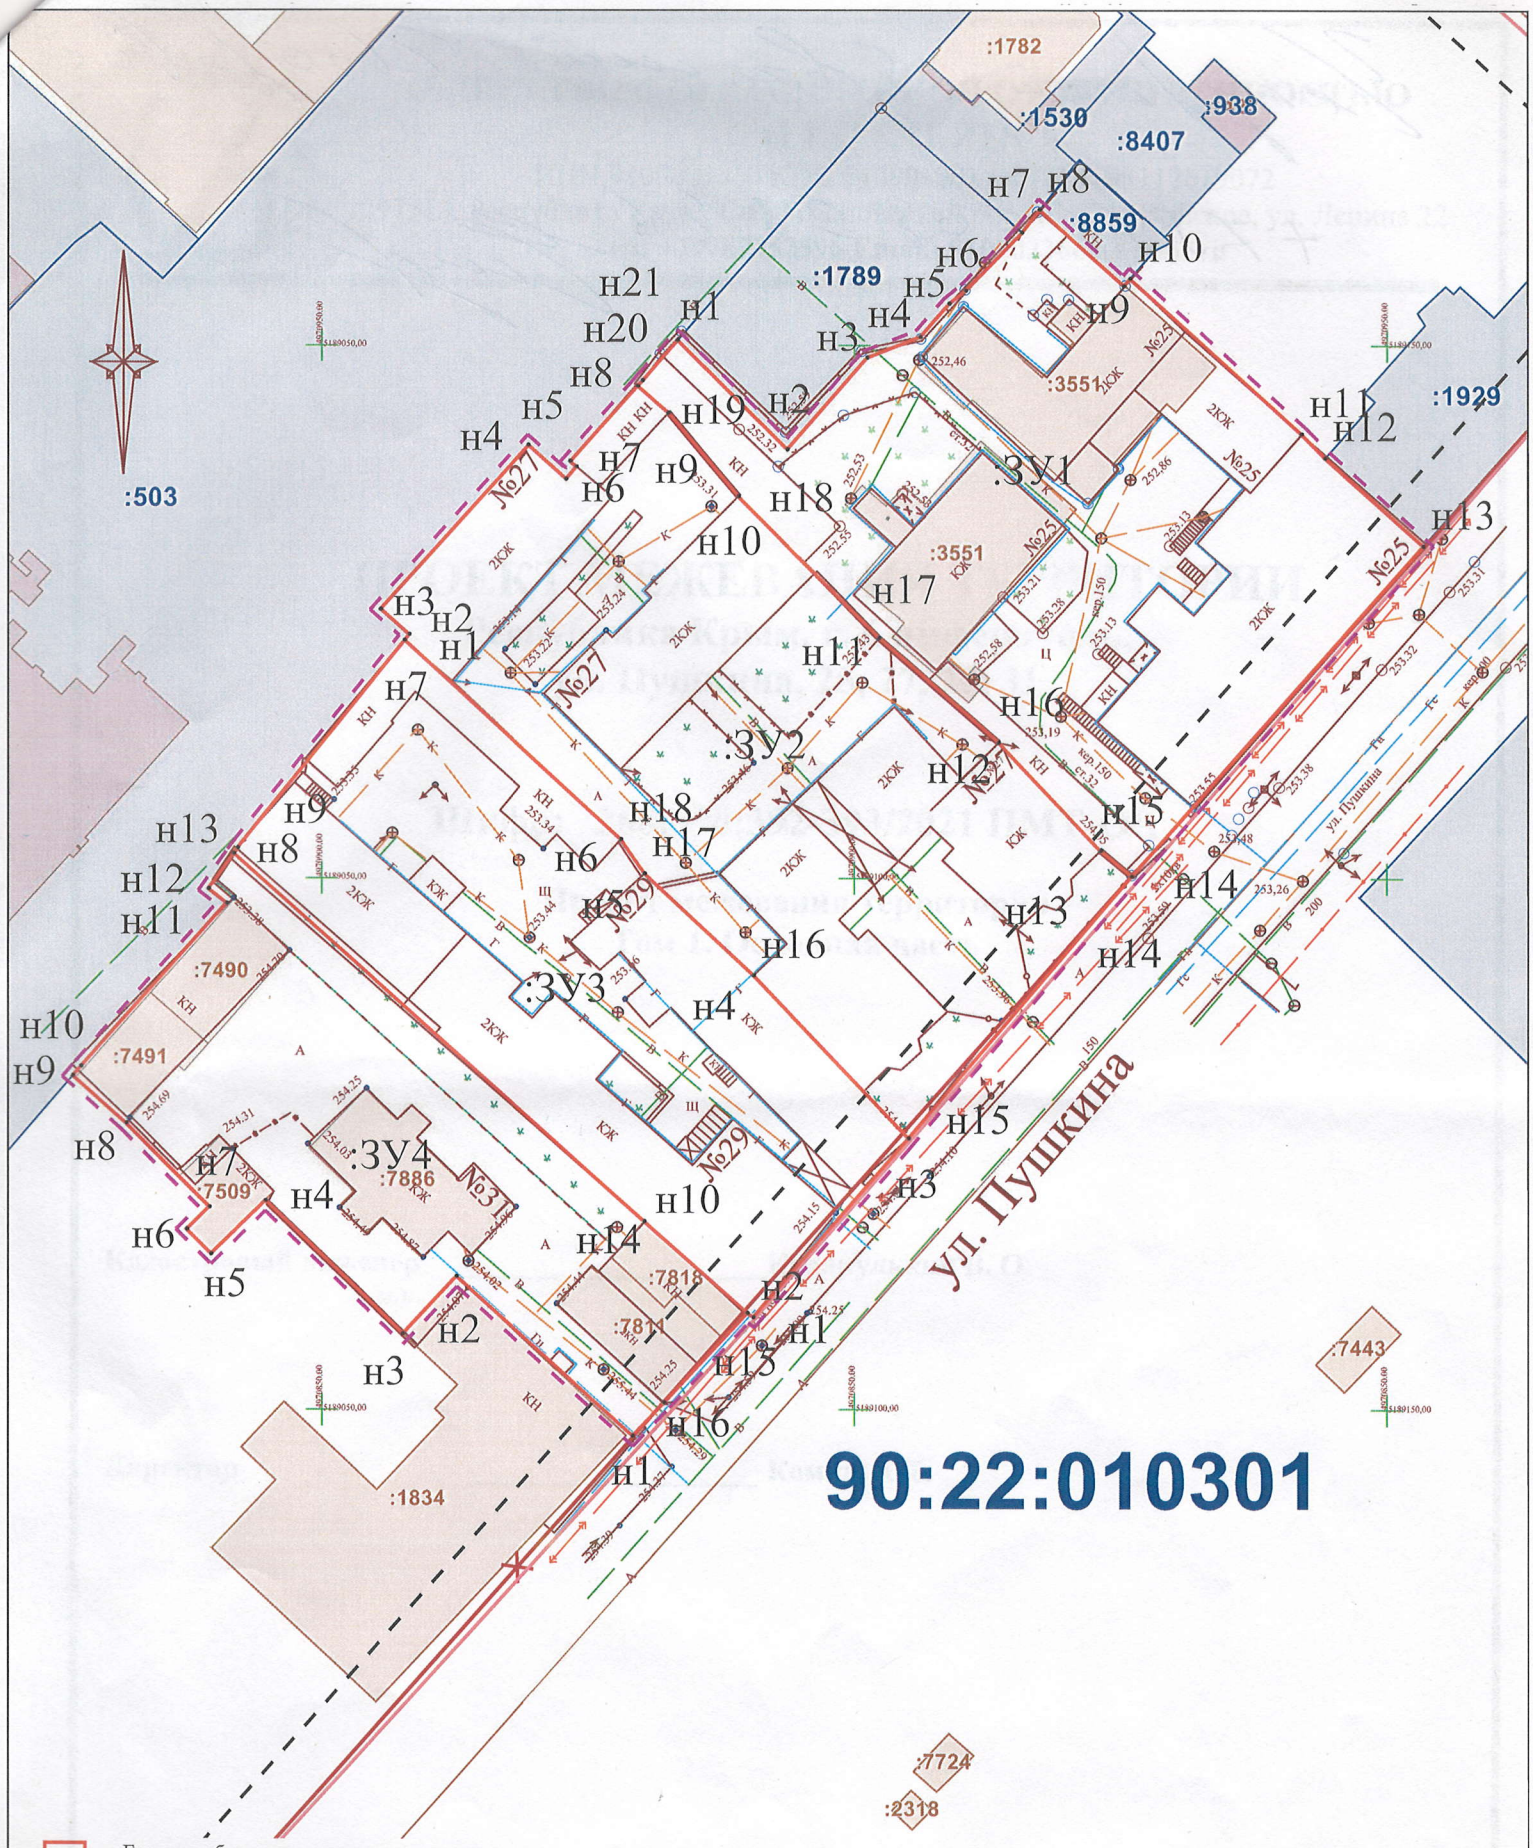


- Границы образуемых земельных участков;
- Граница проектируемой территории;
- Проектируемая красная линия;
- Прекращающая существование красная линия;
- Красная линия;
- Линии отступа от красных линий в целях определения мест допустимого размещения ОКС;
- Граница кадастрового квартала;

		Подпись		
Директор	Комшу К.Т.			
Выполнил	Каракулькин В.О.			

Республика Крым, г. Симферополь, ул. Пушкина 25, 27, 29, 31
388; 390; 392-393/2021 ПМТ-ОЧ-ГЧ

Чертёж территории межевания Образуемые земельные участки	Масштаб	Лист	Листов
	1:500	2	2
Система координат СК-63 Система высот-Балтийская	ООО "ГЕОАЛЬЯНС"		